B TECHNICA · DEMO
K-101 — Rzut stropu nad parterem

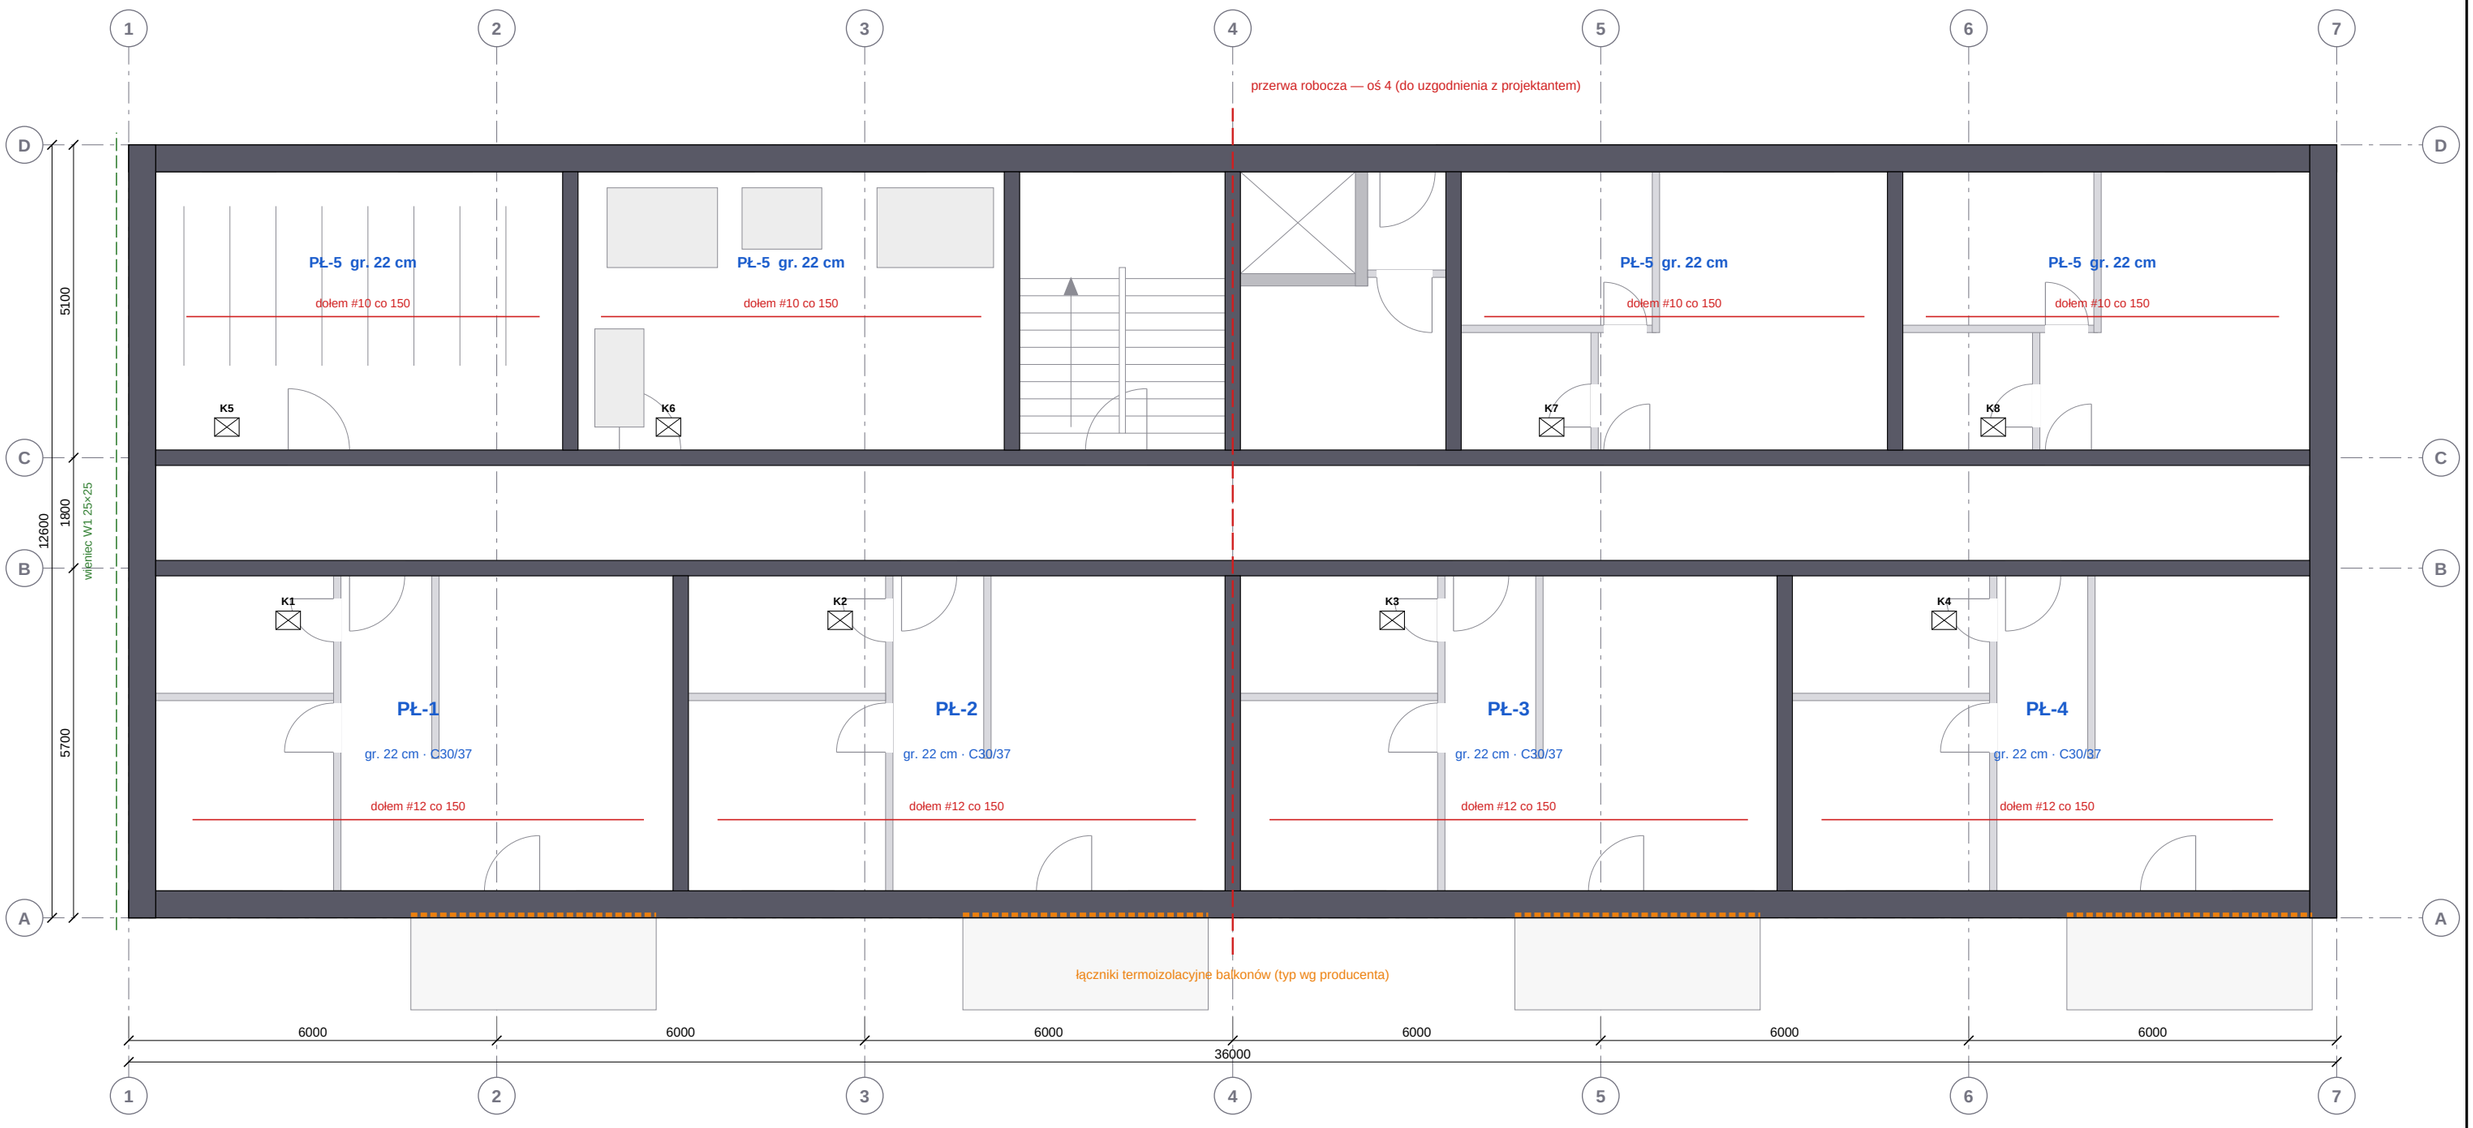

Konstrukcja — uwagi

1. Strop płytowy żelbetowy gr. 22 cm, beton C30/37 XC1, stal B500SP, otulina 25 mm.
2. Otwory K1–K8 pod piony kanalizacyjne 40×30 cm — lokalizacja wg branży sanitarnej.
3. Rozdeskowanie stropu po osiągnięciu 70% wytrzymałości (potwierdzenie badaniem).

Rew.	Opis zmiany	Data
A	Wydanie do realizacji	2026-02-16
B	Otwory pod piony K1–K8	2026-03-11

Osiedle Zielone Tarasy — Etap I · Budynek A
Inwestor: Zielone Tarasy Development Sp. z o.o. (podmiot fikcyjny)

Rzut stropu nad parterem

Konstrukcja · strop płytowy gr. 22 cm

Nr rysunku	Skala	Rewizja	Data
K-101	1:100	B	2026-03-11

Branża: Konstrukcja
Faza: projekt wykonawczy

Projektował: inż. K. Nowicki
Sprawdził: arch. J. Czarnecka

DANE DEMONSTRACYJNE — RYSUNEK FIKCYJNY, NIE DO BUDOWY